


June 15, 2014 4:33:31 p.m.
Drawing LISTENINGSLACONTRACT DOCUMENTS\TITLE BLOCKS\REV\CD\468047.DWG

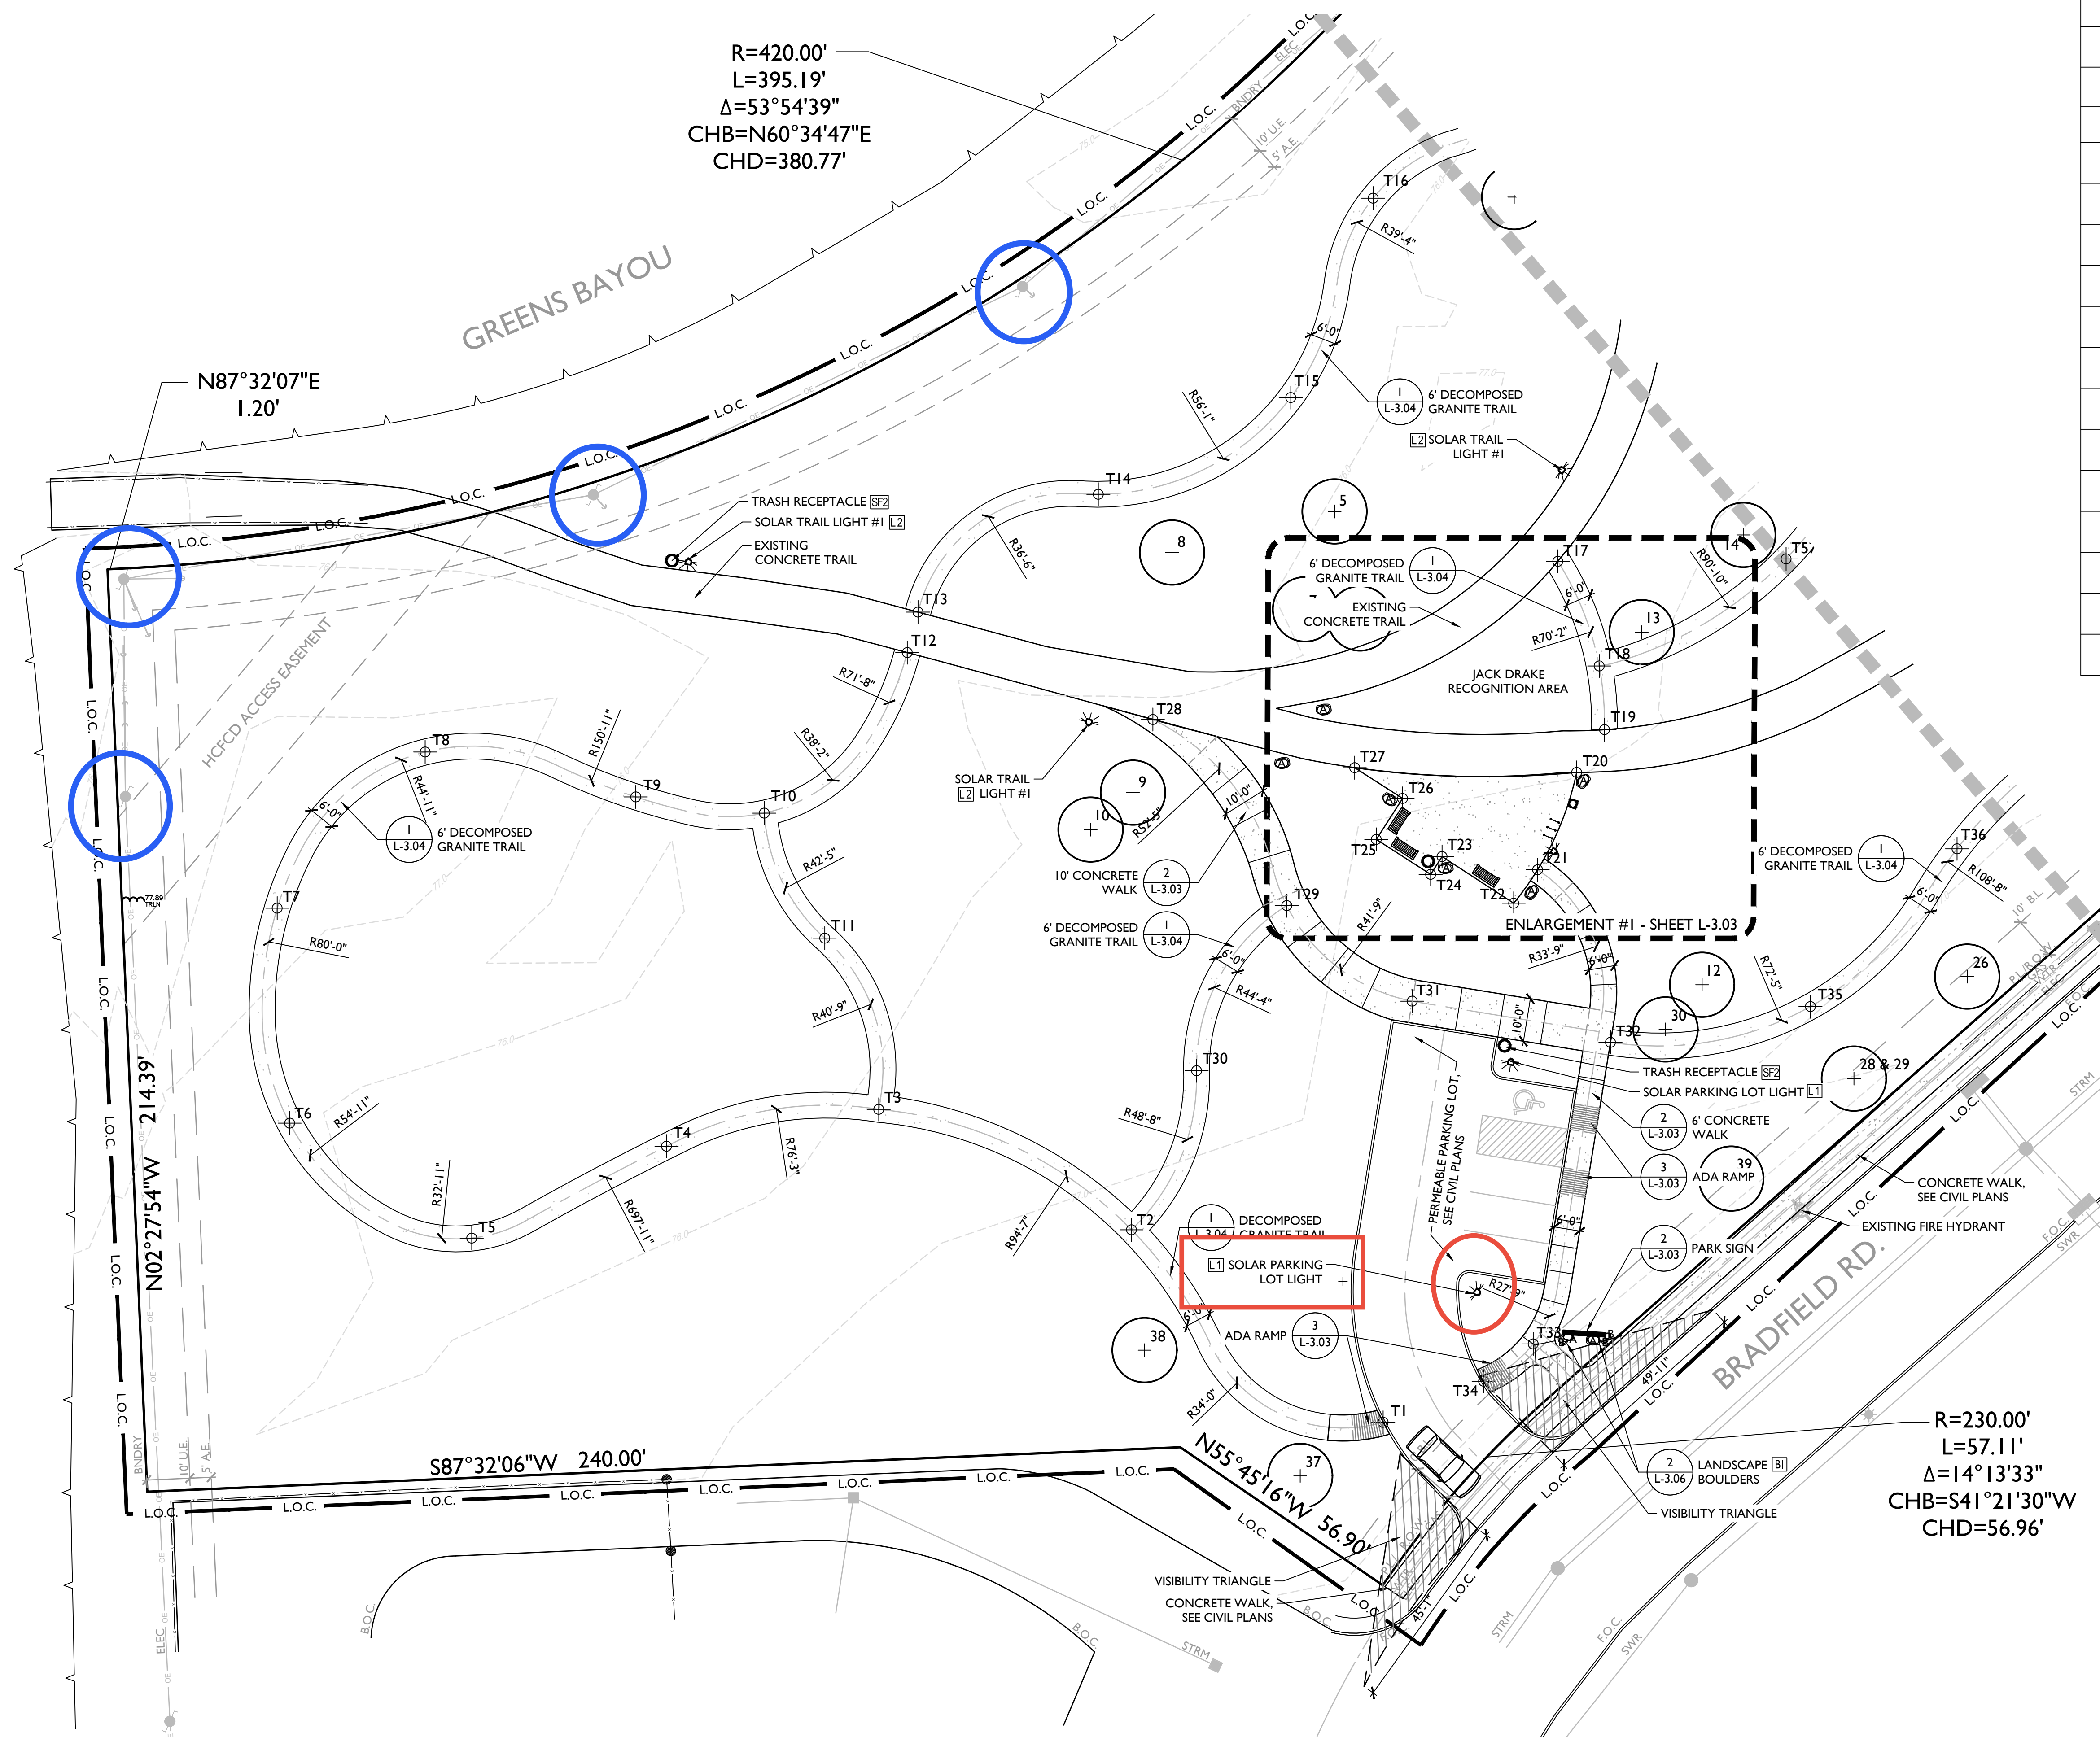


TRAIL COORDINATE CONTROLS					
	X 311...	Y 139...		X 311...	Y 139...
T1	...2164.70	...09694.57	T19	...2216.10	...09855.40
T2	...2106.29	...09739.28	T20	...2209.64	...09845.47
T3	...2047.62	...09767.24	T21	...2200.57	...09822.87
T4	...1998.35	...09758.68	T22	...2195.02	...09815.10
T5	...1953.14	...09737.34	T23	...2178.38	...09825.93
T6	...1910.87	...09764.04	T24	...2175.73	...09821.81
T7	...1907.98	...09813.96	T25	...2163.11	...09829.92
T8	...1942.33	...09850.22	T26	...2169.22	...09839.43
T9	...1991.22	...09839.78	T27	...2158.11	...09846.57
T10	...2021.05	...09836.03	T28	...2111.25	...09857.76
T11	...2035.08	...09806.99	T29	...2142.33	...09814.55
T12	...2054.24	...09873.31	T30	...2121.40	...09776.21
T13	...2056.74	...09882.71	T31	...2171.46	...09792.35
T14	...2098.59	...09910.06	T32	...2217.48	...09782.81
T15	...2143.26	...09932.52	T33	...2199.55	...09712.78
T16	...2162.38	...09978.80	T34	...2188.04	...09704.11
T17	...2205.27	...09894.50	T35	...2263.90	...09791.11
T18	...2214.87	...09870.19	T36	...2297.93	...09827.75

LEGEND

- P.O.B. POINT OF BEGINNING
- T9 TRAIL COORDINATE POINT

KEY MAP

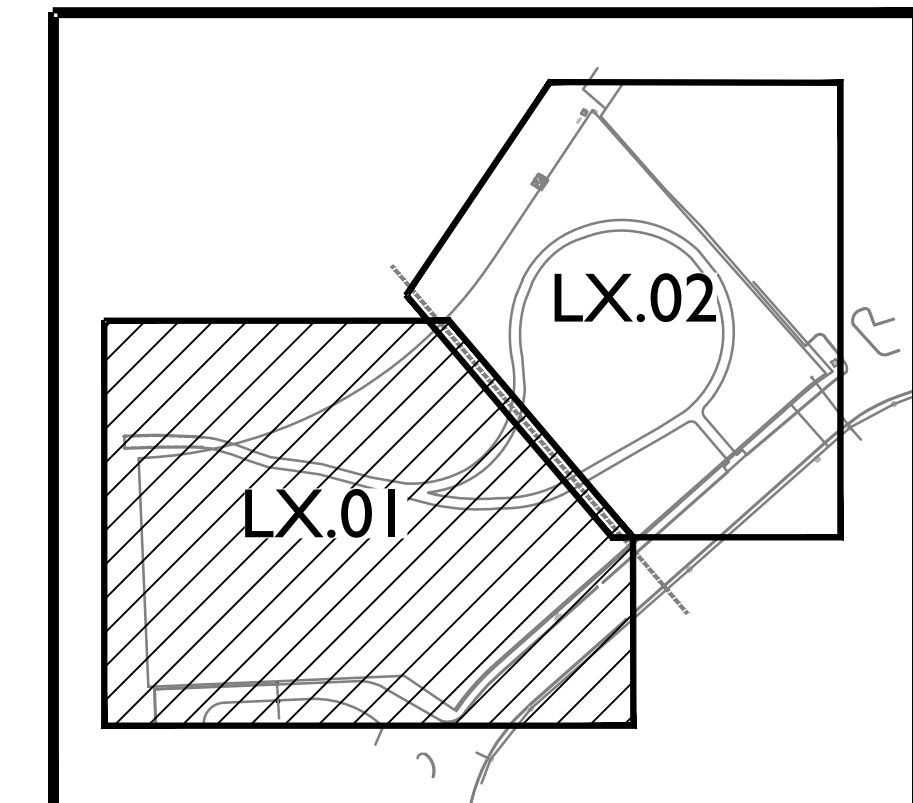

SCALE: 1" = 20'
0 10 20 40



19 Briar Hollow Lane, Suite 145
Houston, Texas 77027
(713) 621-8025



JACK DRAKE PARK Houston, TX LANDSCAPE ARCHITECTURE PLANS

PROJECT NO.: 133940.1
DATE: 08/30/2016
DRW: MM, RW
RVW: RW, JH

ISSUED
FOR BID - 08/30/2016

Hardscape
Plan

L-3.01