


1/16" = 1' (SEE NOTE 1)
DATE: 08/30/2016
DRAWN: RHL/RY
CHECKED: RHL/RY

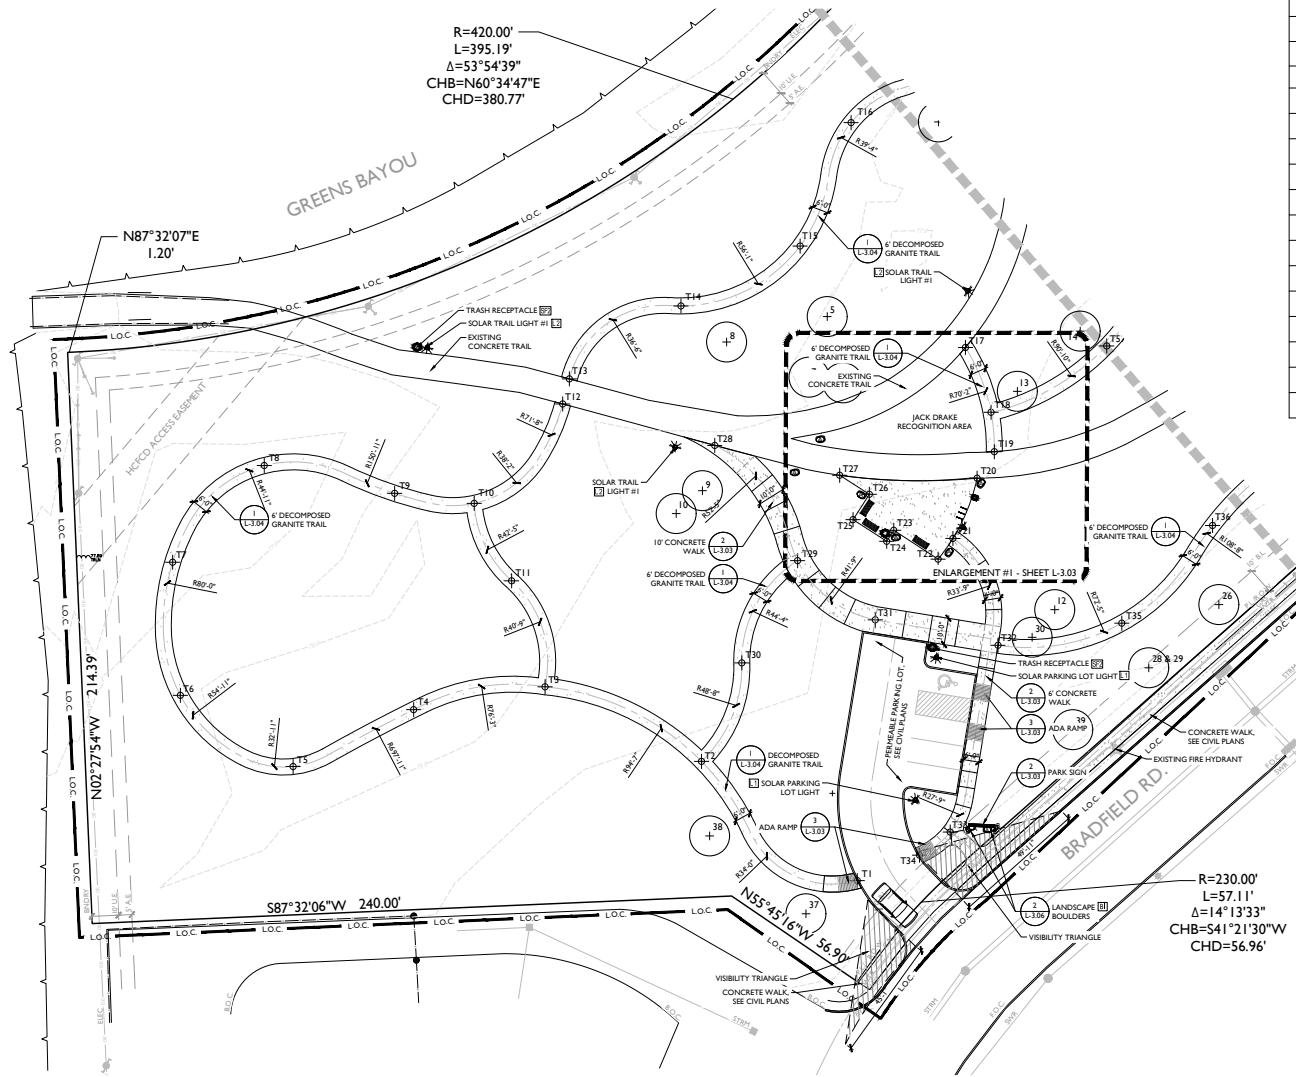

R=420.00'
L=395.19'
Δ=53°54'39"
CHB=N60°34'47"E
CHD=380.77'

N87°32'07"E
1.20'

N02°27'54"W 214.39'

S87°32'06"W 240.00'

R=230.00'
L=57.11'
Δ=14°13'33"
CHB=S41°21'30"W
CHD=56.96'


TRAIL COORDINATE CONTROLS

	X 311...	Y 139...		X 311...	Y 139...
T1	...2164.70	...09694.57	T19	...2216.10	...09855.40
T2	...2106.29	...09739.28	T20	...2209.64	...09845.47
T3	...2047.62	...09767.24	T21	...2200.57	...09822.87
T4	...1998.35	...09758.68	T22	...2195.02	...09815.10
T5	...1953.14	...09737.34	T23	...2178.38	...09825.93
T6	...1910.87	...09764.04	T24	...2175.73	...09821.81
T7	...1907.98	...09813.96	T25	...2163.11	...09829.92
T8	...1942.33	...09850.22	T26	...2160.22	...09839.43
T9	...1991.22	...09839.78	T27	...2158.11	...09846.57
T10	...2021.05	...09836.03	T28	...2111.25	...09857.76
T11	...2035.08	...09806.99	T29	...2142.33	...09814.55
T12	...2054.24	...09873.31	T30	...2121.40	...09776.21
T13	...2056.74	...09882.71	T31	...2171.46	...09792.35
T14	...2098.59	...09910.06	T32	...2217.48	...09782.81
T15	...2143.26	...09932.52	T33	...2199.55	...09712.78
T16	...2162.38	...09978.80	T34	...2188.04	...09704.11
T17	...2205.27	...09894.50	T35	...2263.90	...09791.11
T18	...2214.87	...09870.19	T36	...2297.93	...09827.75

LEGEND

- POINT OF BEGINNING
- TRAIL COORDINATE POINT

KEY MAP

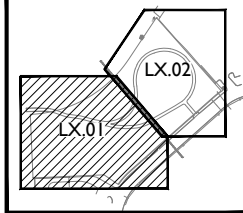

SCALE: 1" = 20'
0 10 20 40



JACK DRAKE PARK
Houston, TX
LANDSCAPE ARCHITECTURE PLANS

PROJECT NO: 133940.1
DATE: 08/30/2016
DRAW: RHL/RY
CHECK: RHL/RY

Hardscape Plan

L-3.01